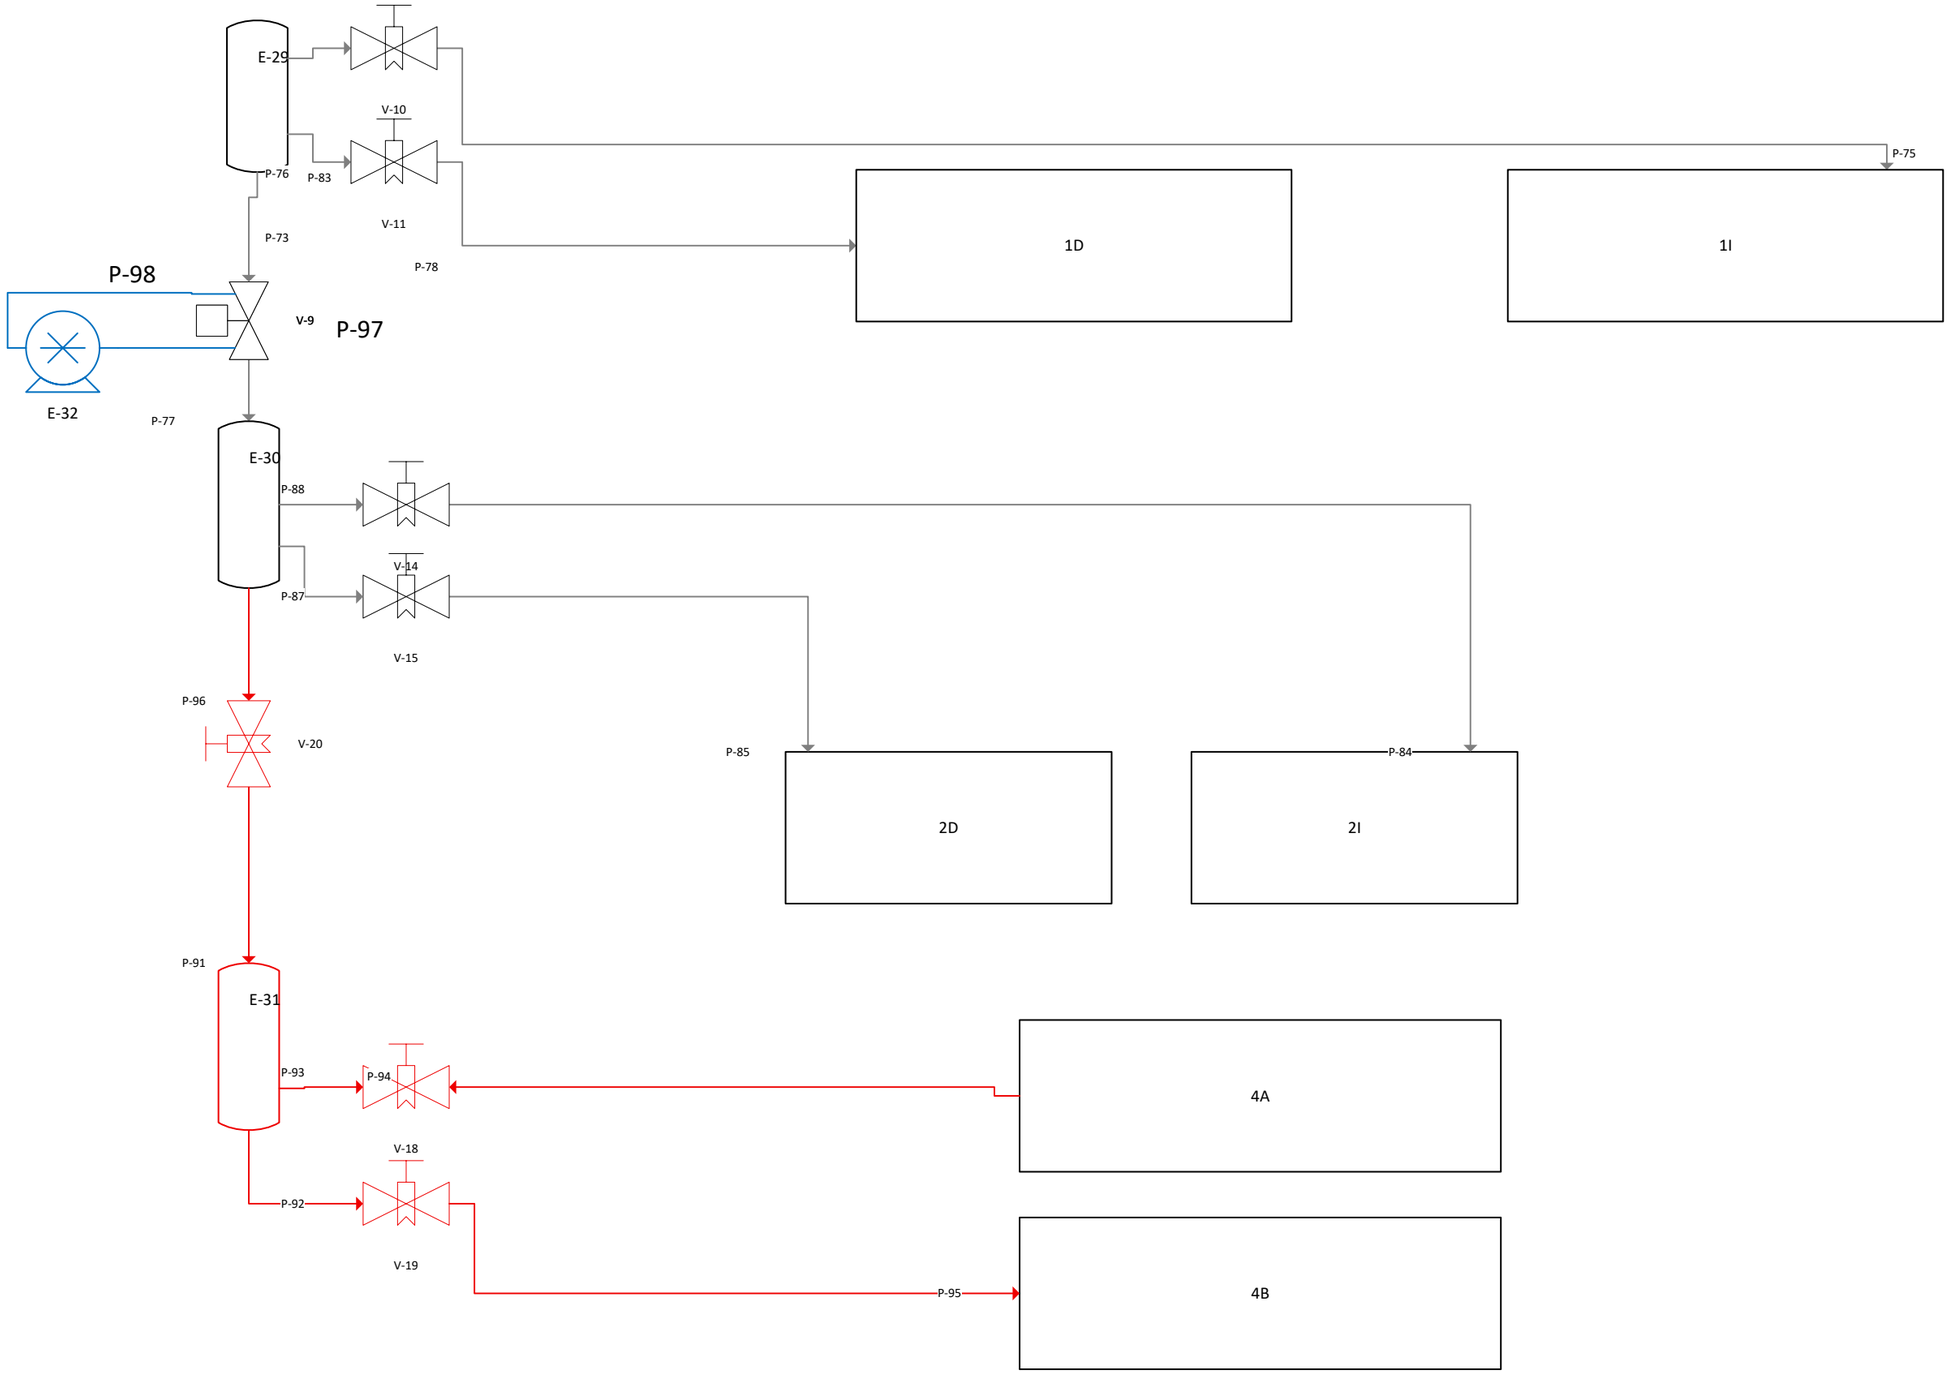
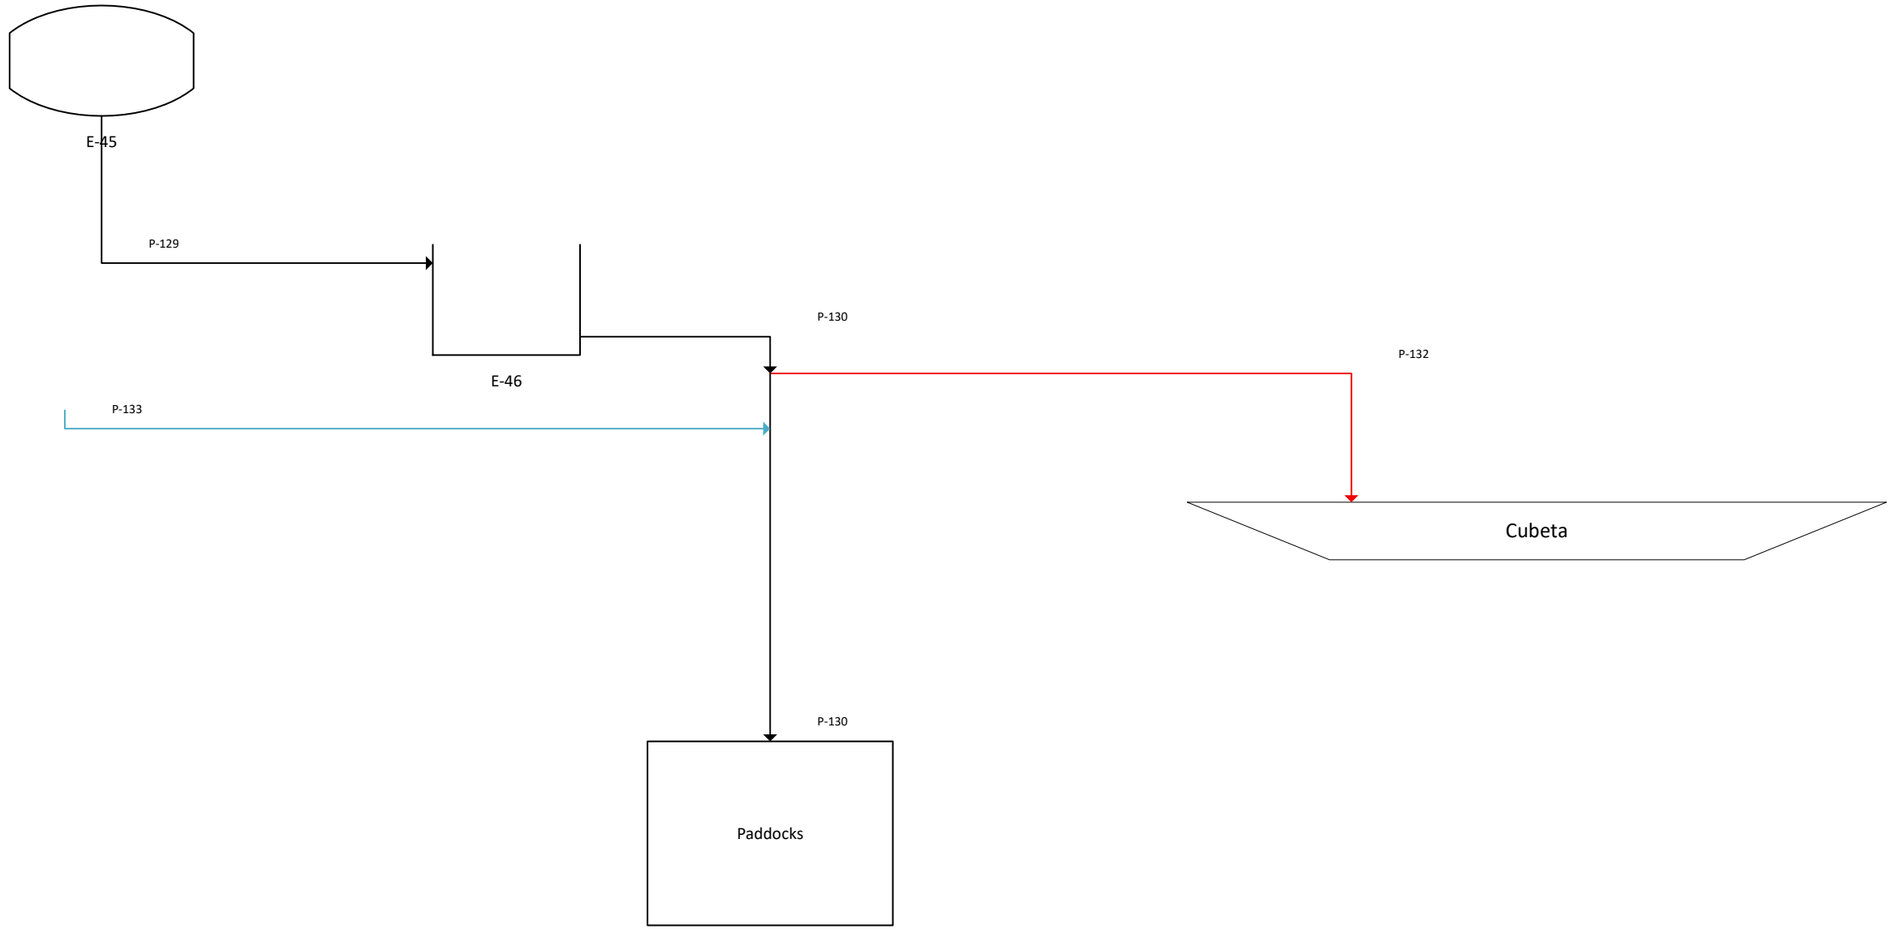
P-40
P-38
P-39
P-37
E-23
P-11
Cajón de dilusión
P-35
P-36
CONCENTRADORA
E-19
E-20
E-17
P-5
P-4
BHC-1
Cajón de lamas
Emergencia
20"
48"
36"
28"
P-34
P-33
E-16
E-14
P-3
P-2
BHC-2
P-6
Cajón de arenas
P-1
51
20"
81
20"
P-31
Nodo 1
16"
24"
20"
Manifold
Cubeta
E-18
10"
10"
10"
8"
8"
Nodo 2
V-3
V-4
16"
1D
1I
16"
P-51
P-52
V-5
20"
V-29
P-135
P-136
P-41
P-42
Nodo 3
2D
2I
20"
V-30
4A
4B
P-142
PL P-45
Global 12GHH 02
PL 2
P-46
P-140
Sumidero
PL 3
PL 4
P-47
P-48
P-139
P-144
Godwin 160
B09
P-143
Shearkey
P-138
P-141
Global 12GHH 03
Godwin 160
B15
P-50
Seepage 1
Piscina 3
Emergencia
P-32
Sepage 2


E-29
V-10
P-76
P-83
V-11
P-73
P-78
P-98
V-9
P-97
E-32
P-77
E-30
P-88
V-14
P-87
V-15
P-96
V-20
P-91
E-31
P-93
P-94
V-18
P-92
V-19
P-95
P-85
P-84
P-75
1D
1I
2D
2I
4A
4B


E-45
P-129
E-46
P-130
P-132
P-133
Cubeta
P-130
Paddocks